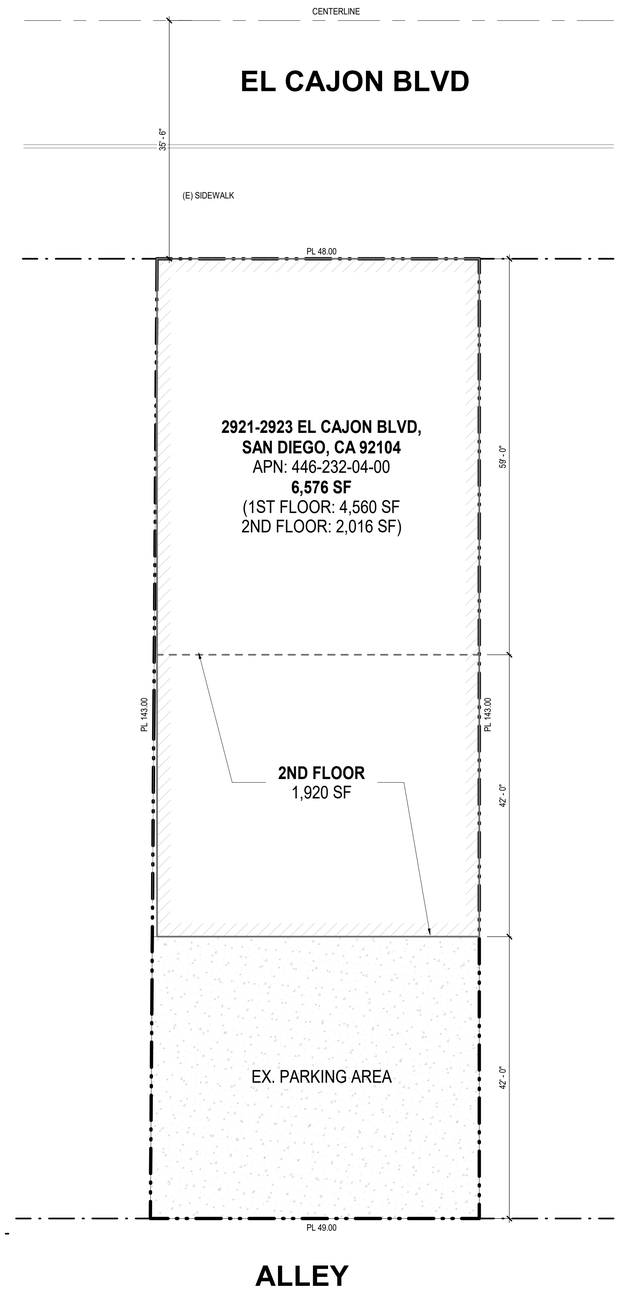

1 EXISTING SITE PLAN
1" = 10'-0"

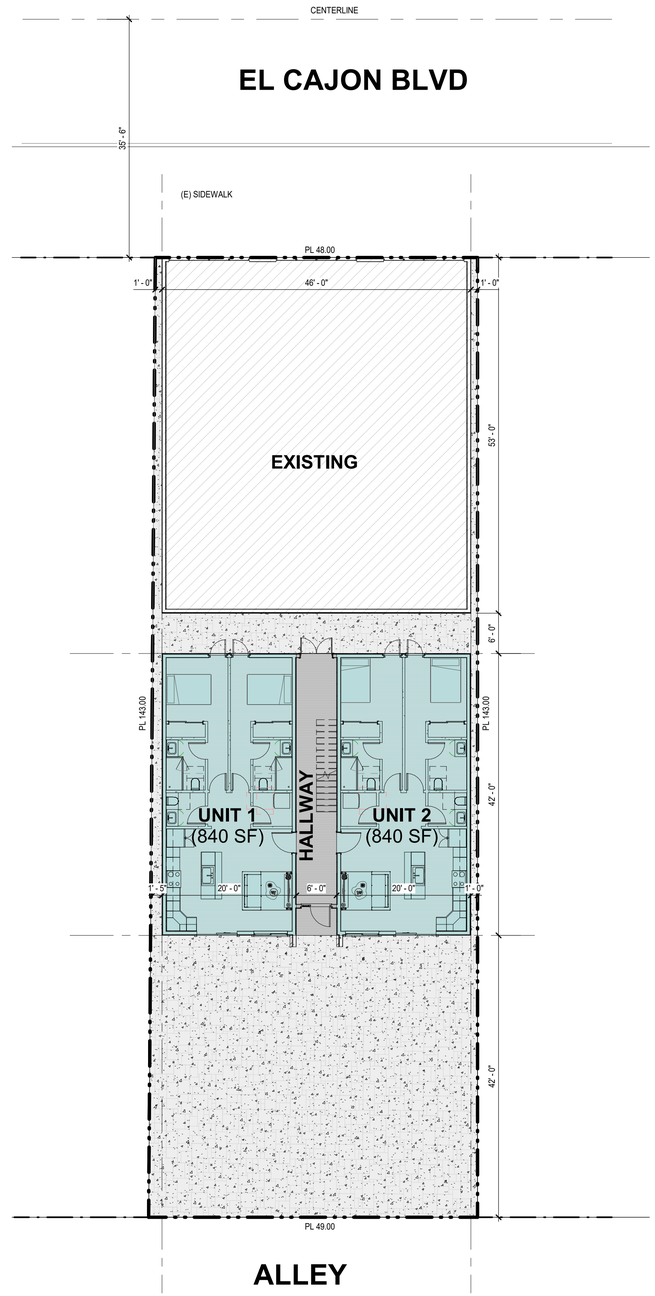

2 PROPOSED 1 ST FLOOR PLAN
1" = 10'-0"

PROJECT DATA

1.	PROJECT NAME	MIX-USED DEVELOPMENT
2.	PROJECT ADDRESS	2921-2923 EL CAJON BLVD, SAN DIEGO, CA 92104
3.	PROJECT OWNER	--
4.	ACCESSOR'S PARCEL NUMBER	446-232-04-00
5.	ZONING	CC-3-9
6.	OCCUPANCY	--
7.	TYPE OF CONSTRUCTION	--
8.	SPRINKLER	--
9.	PARCEL LOT AREA	6,935.55-SF OR 0.159 ACRES
10.	EXISTING BUILDING	6,576-SF
11.	TRANSIT PRIORITY AREA	YES
12.	FLOOD ZONE	X

VICINITY MAP

UNIT TYPES

COLOR	TYPE	UNITS	%
	2 BEDROOM	4	100%

COLOR	TYPE	AREA
	EX. BUILDING	2,438 SF

% SITE COVERAGE

FOOTPRINT AREA	AREA (SF)	% SITE
BUILDING	4,370.00	63
CONCRETE WAL	2,565.55	37
TOTAL	**6,935.55**	**100**

DEVELOPMENT STANDARD

DEVELOPMENT STANDARD	C-3-9 ZONE REQUIREMENTS	PROPOSED EL CAJON BLVD PROJECT	NOTES
LOT SIZE	2,500 SF MIN.	6,935.55 SF	COMPLIES
LOT WIDTH	25.0 FT MIN.	48.0 FT	COMPLIES
FRONT SETBACK			
MIN FRONT SETBACK	--	0	COMPLIES
MAX FRONT SETBACK	10.0 FT		
SIDE SETBACK			
MIN SIDE SETBACK	10.0 FT	1 FT	COMPLIES
OPTIONAL SIDE SETBACK	0		
REAR SETBACK			
MIN REAR SETBACK	10.0 FT	3.5 FT	COMPLIES
OPTIONAL REAR SETBACK	0		
DENSITY	1 UNIT/400SF MAX. (17 UNITS)	4 UNITS	COMPLIES
BUILDING HEIGHT	--	FT	
NUMBER OF STORIES	--	2 STORIES	COMPLIES
LOT COVERAGE	35% MIN.	89%	COMPLIES
FLOOR AREA RATIO	3.0 MAX	1.4	COMPLIES
PARKING	0	0	COMPLIES

PROJECT SUMMARY

	NO.	TYPE	LIVING AREA	HALLWAY &STAIR
FLOOR 1	EX. BUILDING		4,209.00	252.00
	UNIT 1	2 BED	840.00	
	UNIT 2	2 BED	840.00	
	TOTAL		**5,889.00**	
	TOTAL 1ST FLOOR			**6,141.00**
FLOOR 2	EX. BUILDING		1,800.23	252.00
	UNIT 3	2 BED	840.00	
	UNIT 4	2 BED	840.00	
	TOTAL		**3,480.23**	
	TOTAL 2ND FLOOR			**3,732.23**
TOTAL FLOOR AREA				**9,873.23**

SYMBOL LEGEND

EXISTING BUILDING LINE
PROPOSED BUILDING LINE
PROPERTY LINE
LOT LINE
FENCE
CONCRETE WALKWAY

REVISION

ID	DATE	BY

COVER SHEET

MIXED-USE DEVELOPMENT

2921-2923 El Cajon Blvd, San Diego, CA 92104

DATE: *03/30/2026*
SCALE: AS SHOWN
DRAW BY: *T.B*
STAMP:

JOB NO: *#475*
DRAWING NO:

A.00