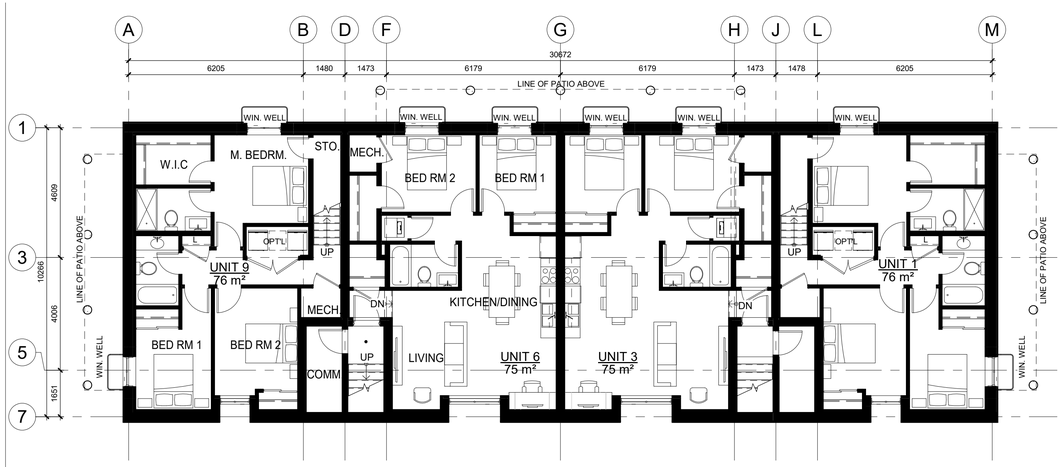

1 A2.1 **BASEMENT FLOOR PLAN**
SCALE: 1 : 100

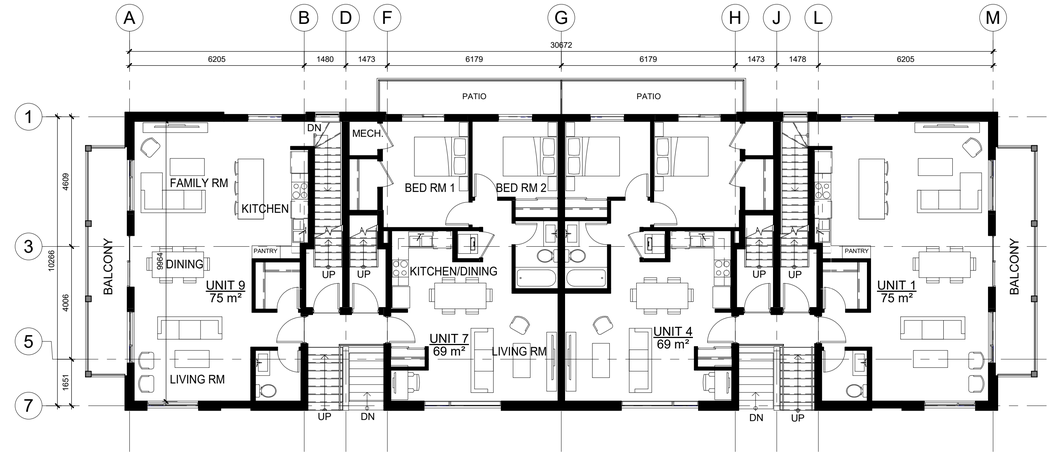

2 A2.1 **FIRST FLOOR PLAN**
SCALE: 1 : 100

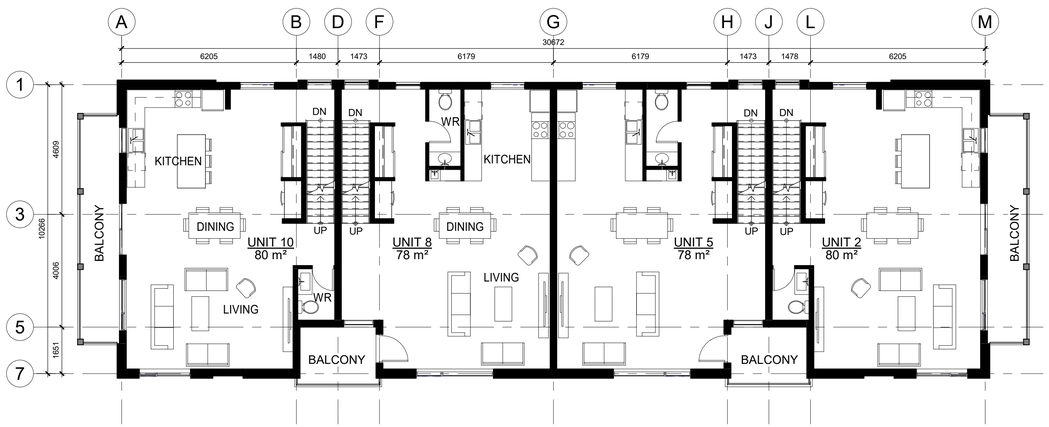

3 A2.1 **SECOND FLOOR PLAN**
SCALE: 1 : 100

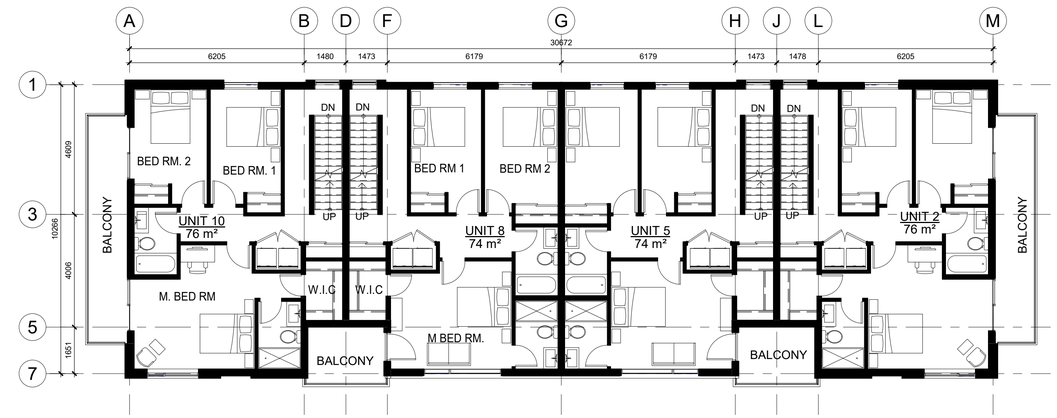

4 A2.1 **THIRD FLOOR PLAN**
SCALE: 1 : 100

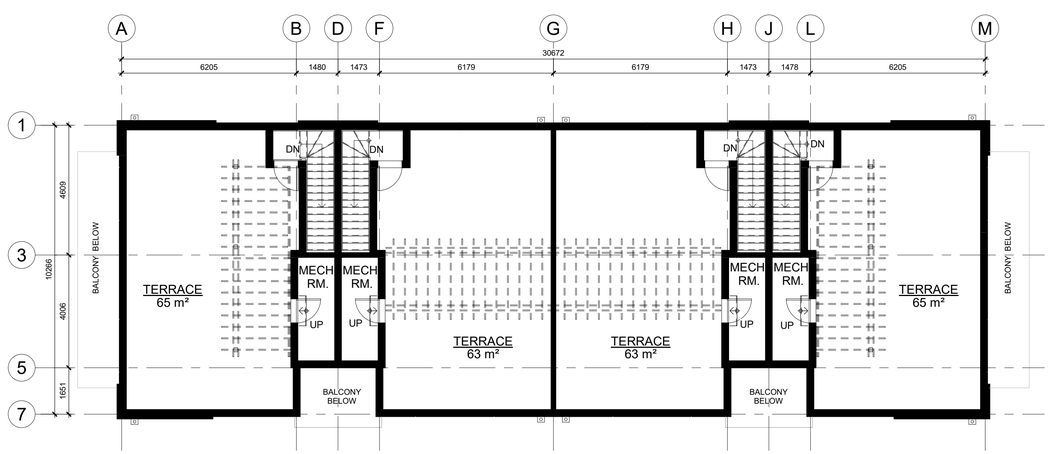

5 A2.1 **TERRACE FLOOR PLAN**
SCALE: 1 : 100

THE CONTRACTOR SHALL VERIFY ALL DIMENSIONS AND REPORT ALL ERRORS AND DISCREPANCIES TO THE CONSULTANT.

THESE DOCUMENTS ARE COPYRIGHTED INSTRUMENTS OF SERVICE AND PROPERTY OF THE ARCHITECT.

THESE DOCUMENTS ARE TO BE USED ONLY ONCE FOR THE INTENDED PURPOSE INDICATED UNDER THE ISSUED DATE.

ANY ALTERATION, DUPLICATION OR COPYING WITHOUT THE CONSENT OF THE ARCHITECT IS PROHIBITED.

DO NOT SCALE THESE DRAWINGS.

REVISIONS:

NO.:	DATE:	ISSUED:

	AREA
UNIT 1	151 m²
UNIT 2	167 m²
UNIT 3	75 m²
UNIT 4	69 m²
UNIT 5	164 m²
UNIT 6	75 m²
UNIT 7	69 m²
UNIT 8	164 m²
UNIT 9	151 m²
UNIT 10	167 m²

MASRI O Inc.
ARCHITECTS
101-609 KUMPF DRIVE
WATERLOO, ON. N2V 1K8
PH. 519.579.0072
www.masrioarchitects.ca.

PROJECT:

STACKED TOWNHOUSE DEVELOPMENT

1154 QUEENS BLVD,
KITCHENER, ONTARIO

Sunset Hills Estates Corporation

DRAWING TITLE:

FLOOR PLANS

DATE: 2023.05.08
SCALE: As indicated
DRAWN: HV
STATUS: SPA
JOB NO.: 2217

DRAWING NO.:

.A2.1

1 .A4.3 **WEST ELEVATION**
SCALE: **1 : 100**

2 .A4.3 **SOUTH ELEVATION**
SCALE: **1 : 100**

3 .A4.3 **EAST ELEVATION**
SCALE: **1 : 100**

4 .A4.3 **NORTH ELEVATION**
SCALE: **1 : 100**

THE CONTRACTOR SHALL VERIFY ALL DIMENSIONS AND REPORT ALL ERRORS AND DISCREPANCIES TO THE CONSULTANT.

THESE DOCUMENTS ARE COPYRIGHTED INSTRUMENTS OF SERVICE AND PROPERTY OF THE ARCHITECT.

THESE DOCUMENTS ARE TO BE USED ONLY ONCE FOR THE INTENDED PURPOSE INDICATED UNDER THE ISSUED DATE.

ANY ALTERATION, DUPLICATION OR COPYING WITHOUT THE CONSENT OF THE ARCHITECT IS PROHIBITED.

DO NOT SCALE THESE DRAWINGS.

REVISIONS:

NO.:	DATE:	ISSUED:

ELEVATION SCHEDULE	
MA	BRICK MASONRY
S 1	SIDING - DARK GREY
S 2	SIDING - LIGHT GREY

MASRI O Inc.
ARCHITECTS
101-609 KUMPF DRIVE
WATERLOO, ON. N2V 1K8
PH. 519.579.0072
www.masrioarchitects.ca.

PROJECT:

STACKED TOWNHOUSE DEVELOPMENT

1154 QUEENS BLVD,
KITCHENER, ONTARIO

Sunset Hills Estates Corporation

DRAWING TITLE:

ELEVATIONS

DATE:	2023.05.08
SCALE:	As indicated
DRAWN:	HV
STATUS:	SPA
JOB NO.:	2217

DRAWING NO.:

.A4.3